


ПАО «СофтЛайн»

**Подключения оборудования
к электросетям**

ООО «АМЕТИСТ КЭПИТАЛ»

Система электроснабжения

2026 год

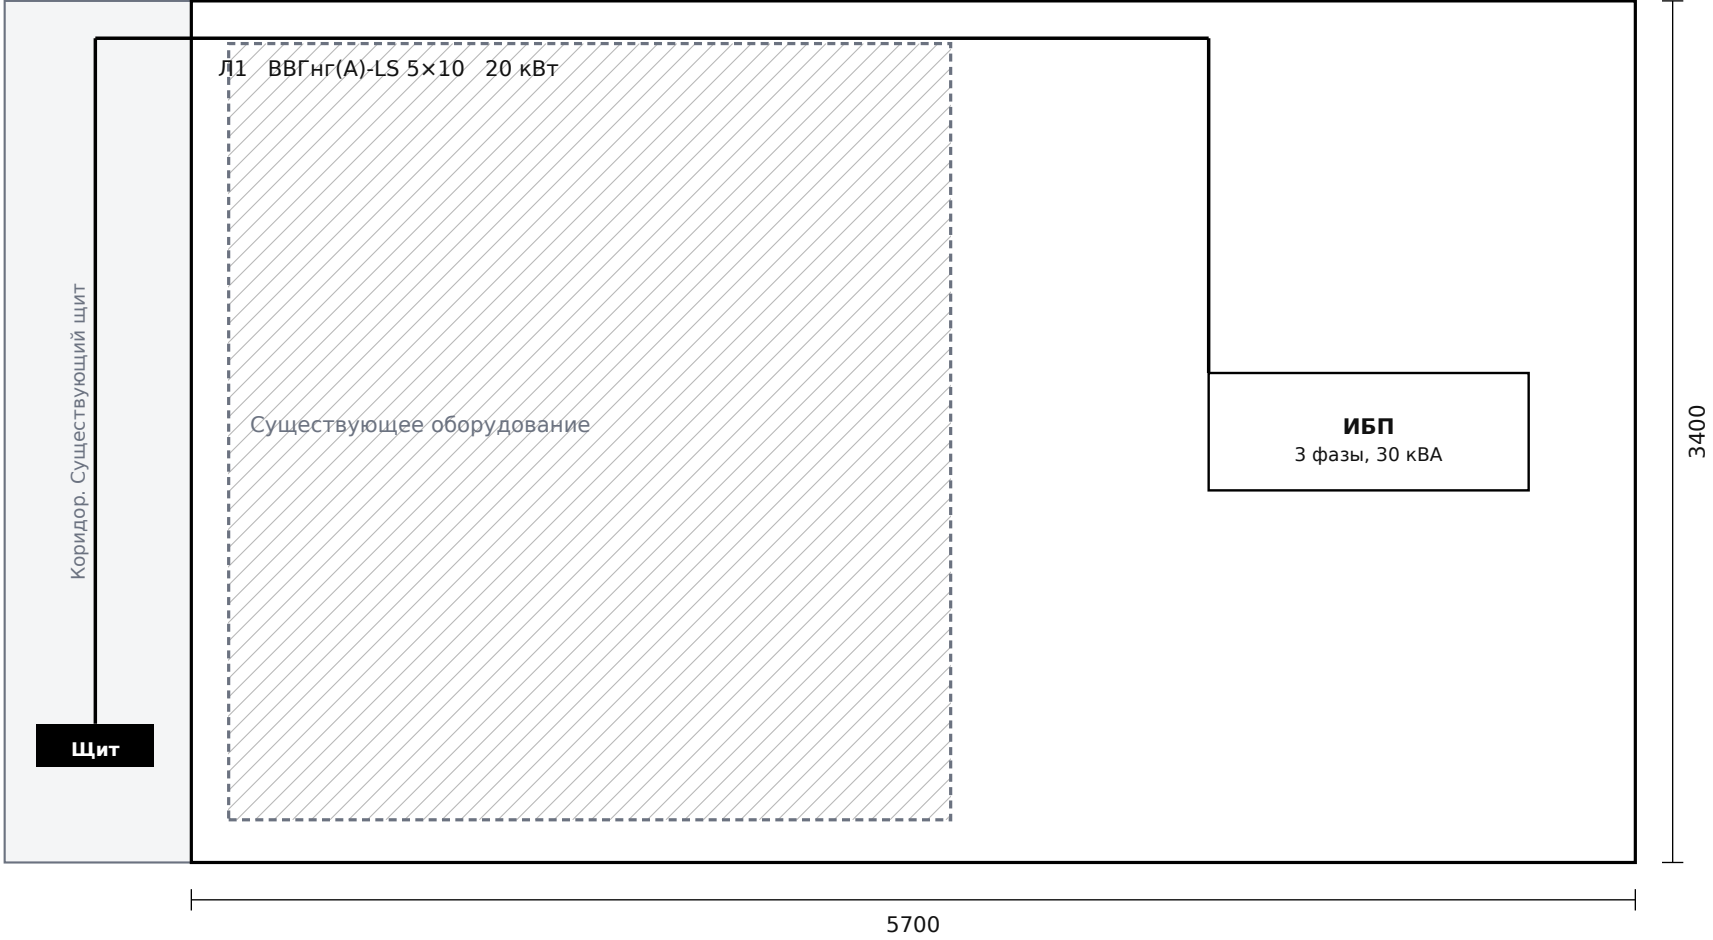


Высота фальшпола 430 мм
Высота фальшпотолка 800 мм
Высота от фальшпола до фальшпотолка 2500 мм

Существующие ИБП и линии — без изменения.

		Подп.	Дата	ООО «АМЕТИСТ КЭПИТАЛ» Подключения оборудования к электросетям ПАО «Софтлайн»		
Разраб.			09.26			
Проверил						
Н. контр.				План расположения оборудования		
				Стадия Р АЗ		
				Лист	2	Листов
					4	

Существующая часть

QF 125 А
ИБП 10 кВА
ИБП 3 кВА
Без изменения

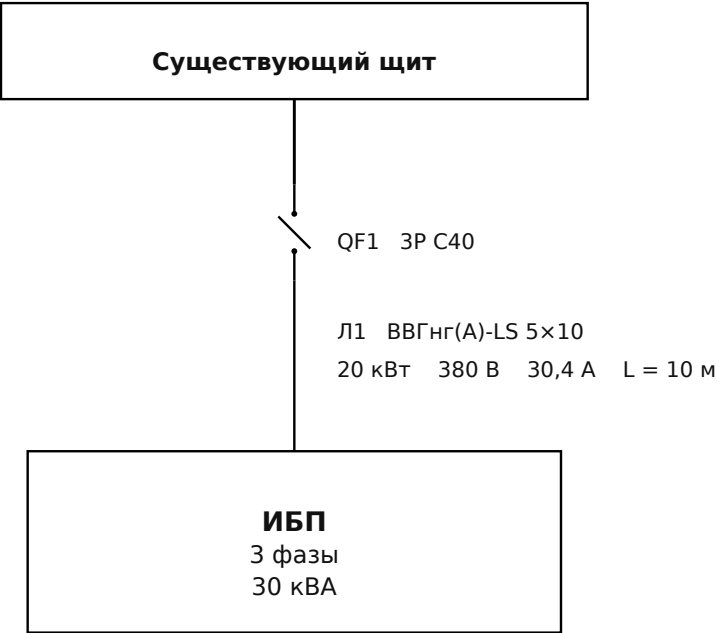

		Подп.	Дата	ООО «АМЕТИСТ КЭПИТАЛ» Подключения оборудования к электросетям ПАО «Софтлайн»		
Разраб.			09.26			
Проверил						
Н. контр.				Схема электроснабжения		
				Стадия Р	Лист 3	Листов 4

Расчет нагрузок

Наименование	L1, кВт	L2, кВт	L3, кВт	P, кВт	cos φ	Kc	Ip, А	U, В	Кабель	L, м
Л1, линия на ИБП	6,67	6,67	6,67	20,00	1,00	1	30,4	380	ВВГнг(А)-LS 5×10	10
Итого	6,67	6,67	6,67	20,00	1,00	1	30,4	380	—	—
Существующие линии	—	—	—	—	—	—	—	—	без изменения	—

Расчет

Линия на трехфазный ИБП.
P = 20 кВт.
cos φ = 1.
U = 380 В.
 $I_p = 20 / (1,73 \times 0,38) = 30,4 \text{ А}$.
Кабель ВВГнг(А)-LS 5×10.
Автомат QF1 3P, хар. С, 40 А.
ИБП 30 кВА, вход 3 фазы, cos φ = 1.
20 кВА < 30 кВА.

		Подп.	Дата	ООО «АМЕТИСТ КЭПИТАЛ» Подключения оборудования к электросетям ПАО «Софтлайн»		
Разраб.			09.26			
Проверил						
Н. контр.				Расчет нагрузок		
				Стадия Р АЗ Лист 4 Листов 4		